


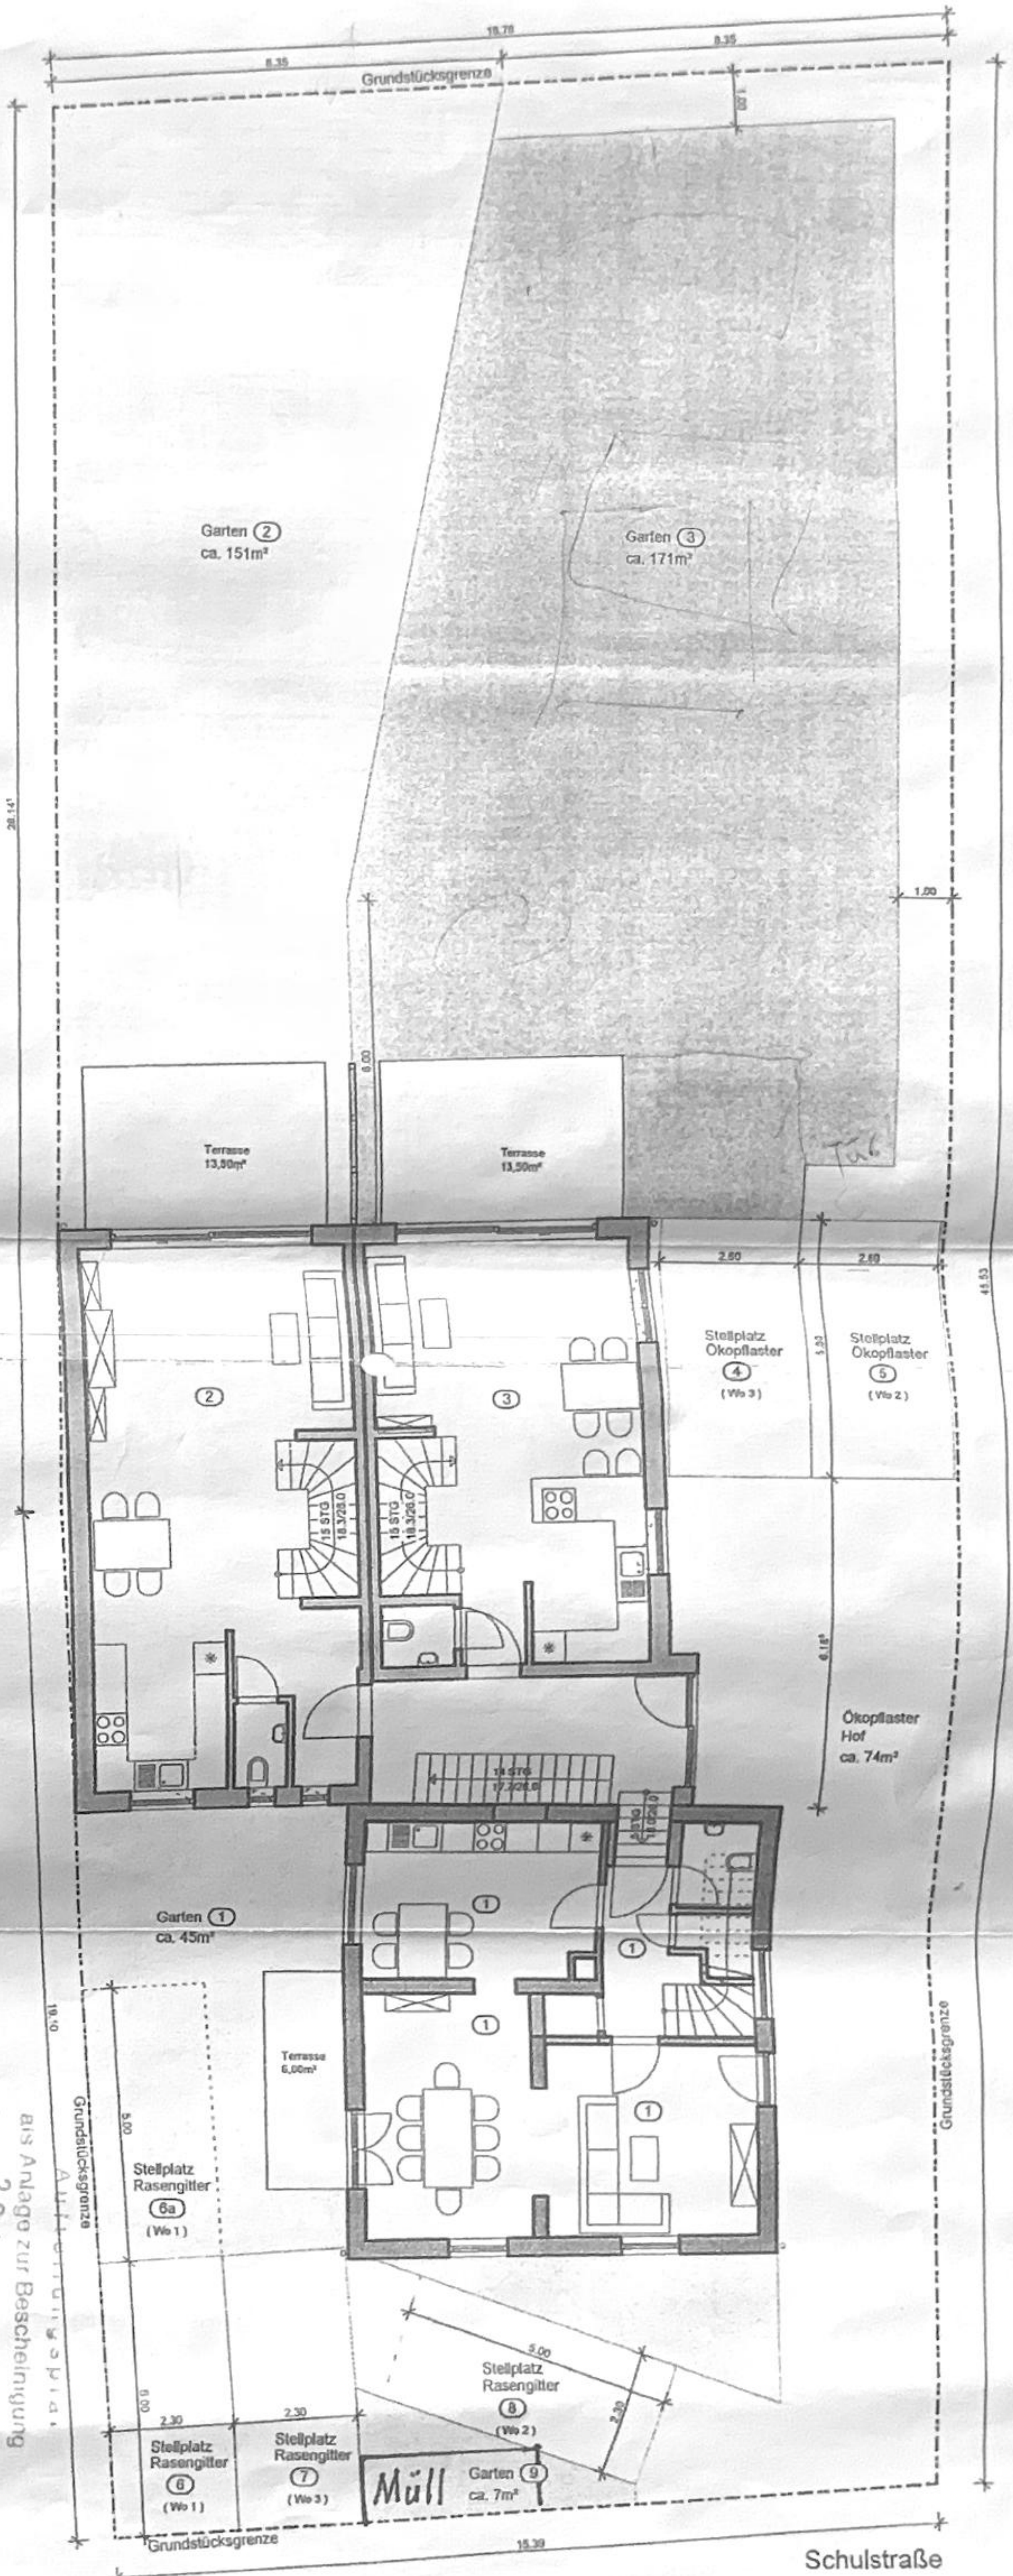

Architekt :

Ruthig

Bauherr :

GT

Bauvorhaben :

Umbau und Neubau eines 3-Familienwohnhauses
Schulstraße 28, 67360 Lingenfeld

Bauherr :

GT Immobilienservice GmbH
Germersheimer Straße 150, 67360 Lingenfeld

Planinhalt :

Eingabeplan Grundstück

Plan Nr.

16 Index :

Projektnr.:

3518-20

Datum : 09.11.2021

Bearb. : Li

Maßstab : 1:125

Bis Anlage zur Bescheinigung
vom 26.11.2021 § 7 Abs. 4
d. Wohnungseigentumsgesetzes
Germersheim, den 26.11.2021
Kreisverordnungsamt
Untere Bräunlestraße 10
67360 Lingenfeld

RUTHIG Ingenieure
Ingenieurbüro für Tragwerksplanung

Dipl.-Ing. (FH) KP Ruthig
Von-Denis-Strasse 7
67346 Speyer
Tel.: 06232-6790680
info@ruthig-ingenieure.de


Az.: 21/21.12.39/11113
 Baurechtschicht geprüft und genehmigt:
 Gemeindevorstand, den 15. Nov. 2021
 Kreisverwaltung
 - Untere Bauaufsichtsbehörde -
 im Auftrag

Handwritten signature

Ausfertigung für den Bauherrn
 als Anlage zur Bescheinigung
 vom 26.09.2021 § 7 Abs. 4
 d. Wohnungseigentumsgesetzes
 Gemeindevorstand, den 15. Nov. 2021
 Kreisverwaltung
 - Untere Bauaufsichtsbehörde -
 im Auftrag



KELLERGESCHOSS M.1:100

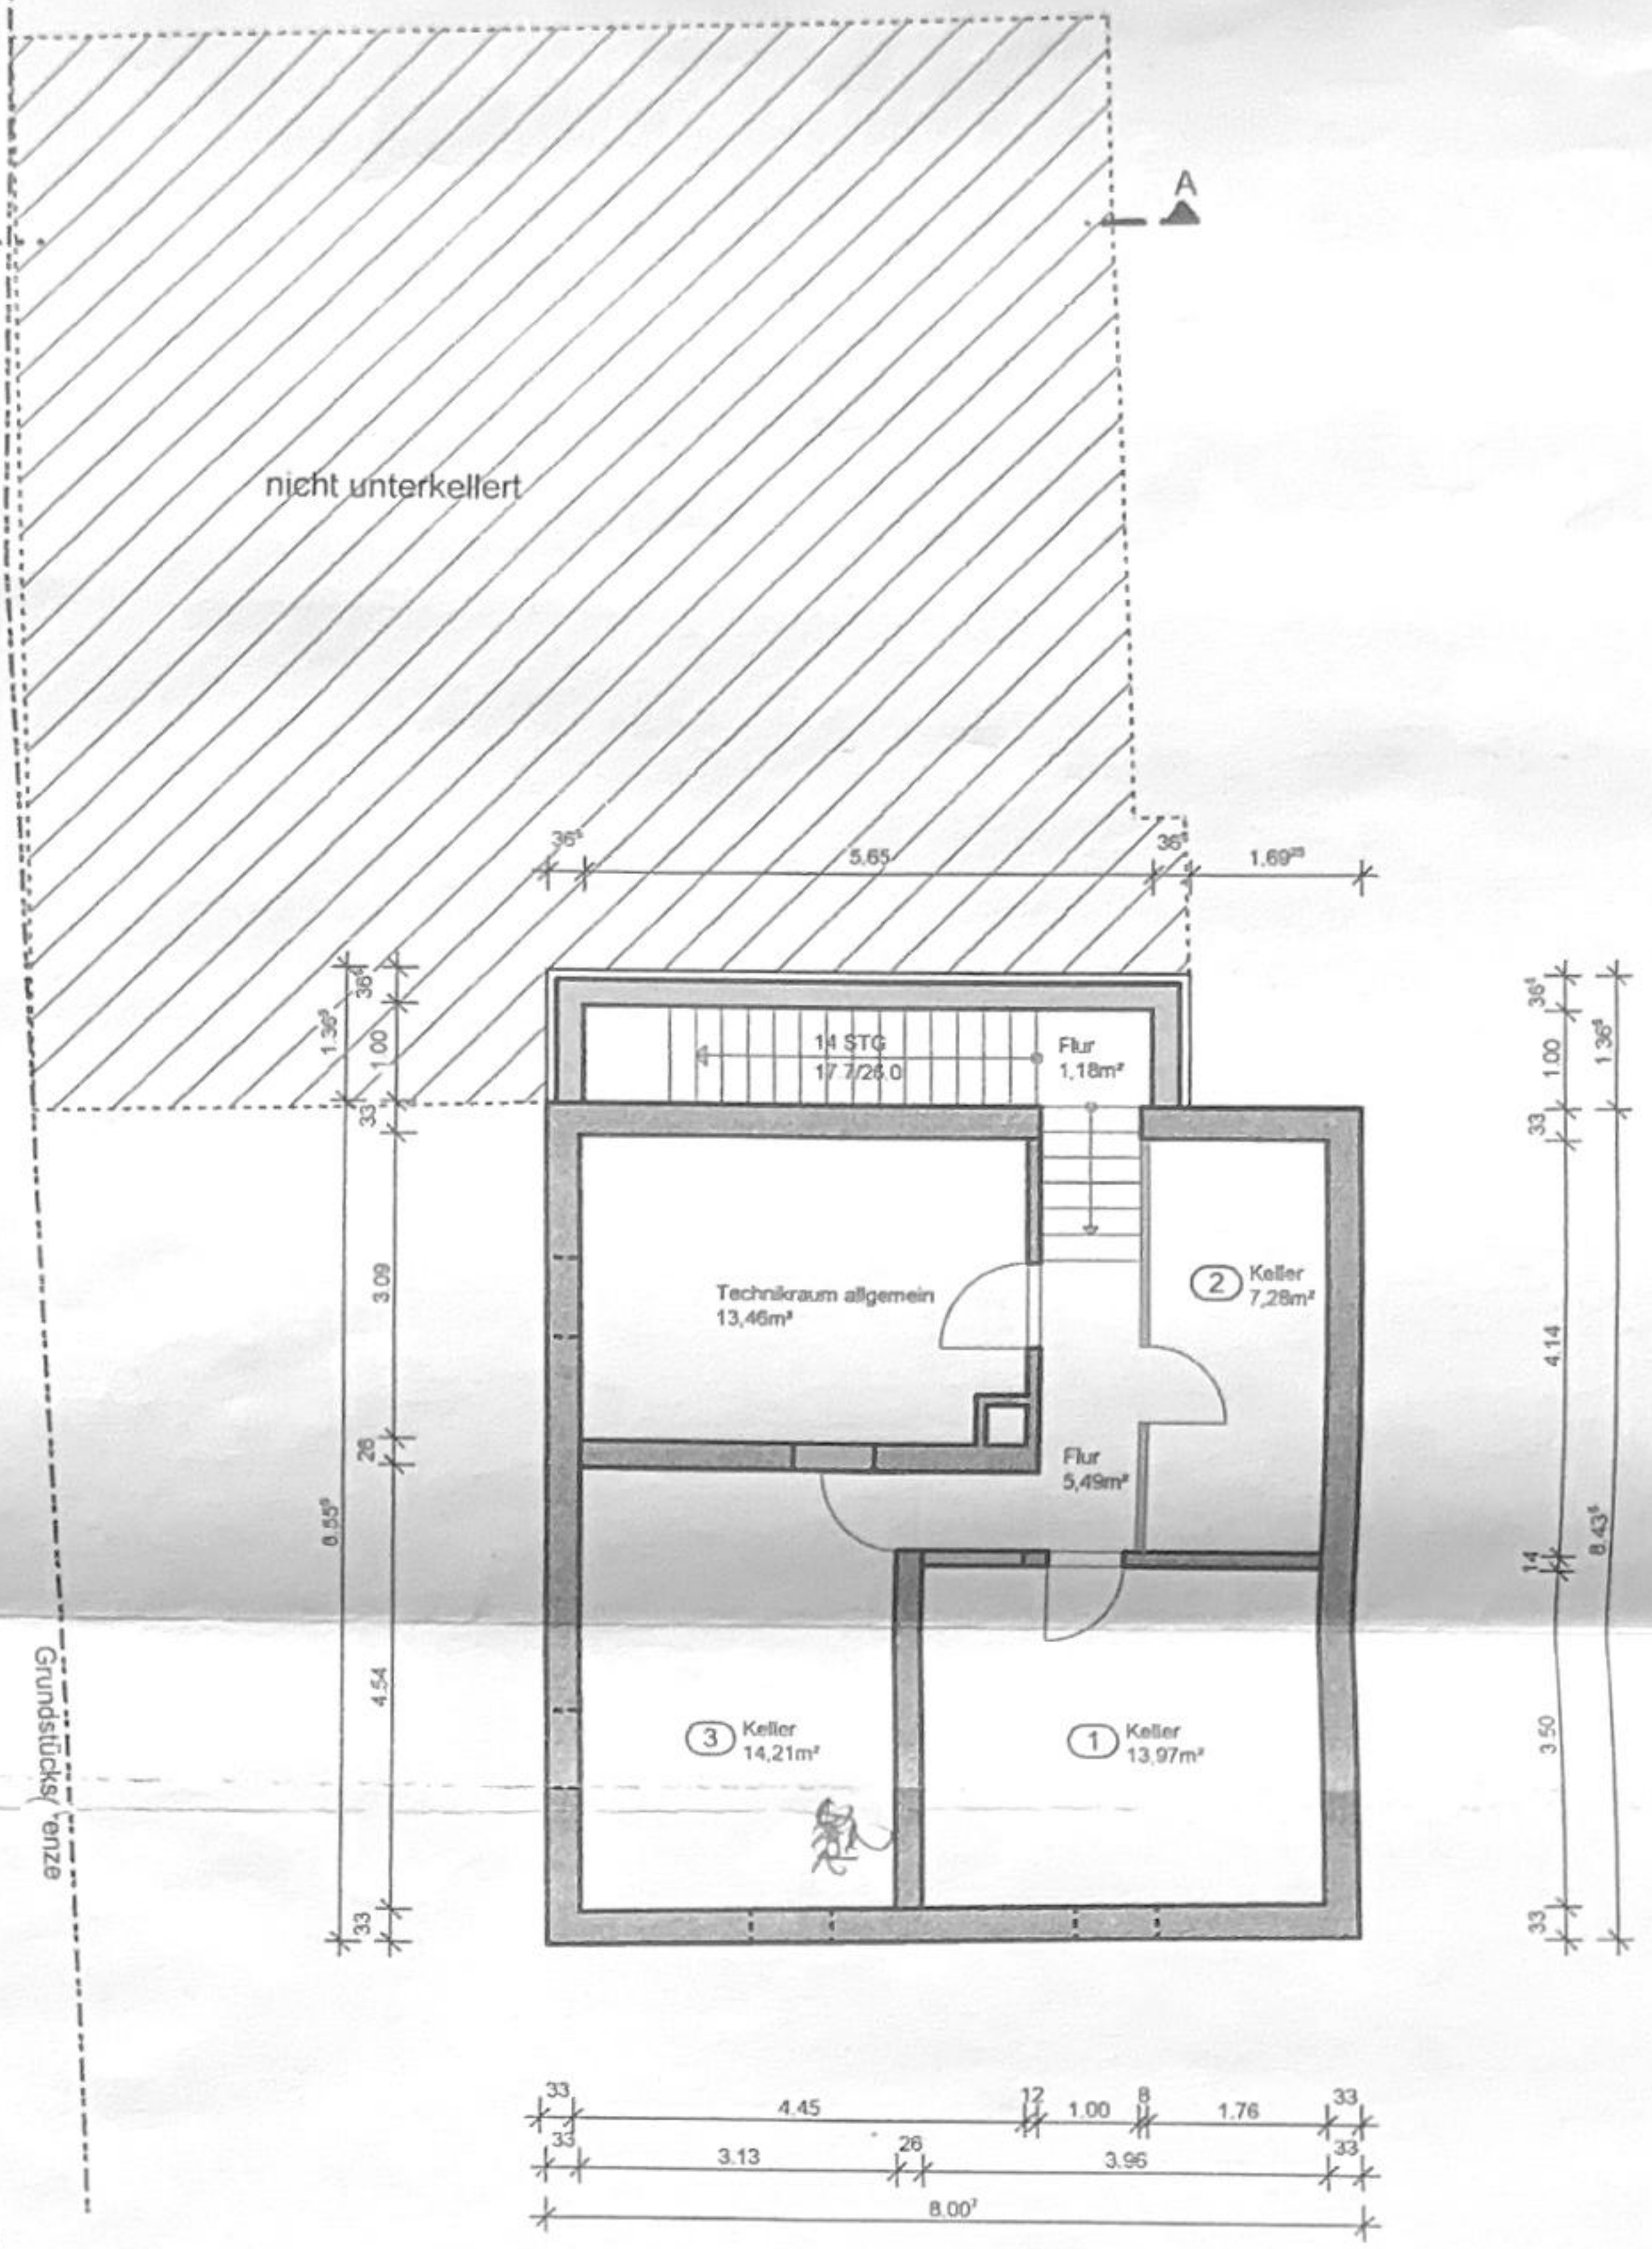

Bauvorhaben :

Umbau und Neubau eines 3-Familienwohnhauses
 Schulstraße 28, 67360 Lingenfeld

Bauherr :

GT Immobilienservice GmbH
 Gemersheimer Straße 150, 67360 Lingenfeld

Planinhalt :

Eingabeplan Grundriss Kellergeschoß

Plan Nr.

10 Index :

Datum : 09.11.2021

Projektnr.:

3518-20

Bearb.: Li
 Maßstab : 1:100

Architekt :

Handwritten signature: Ruthig

RUTHIG Ingenieure
 Ingenieurbüro für Tragwerksplanung


Dipl.-Ing. (FH) KP. Ruthig
 Von-Denis-Strasse 7
 67346 Speyer
 Tel.: 06232-6790680
 info@ruthig-ingenieure.de

2.11.2021
 15. Nov. 2021
 Kreisverteilung
 - Letzte Baugenehmigung -

Aufstellung:
 als Anlage zur Bescheinigung
 vom 2.6. Nov. 2021 § 7 Abs. 4
 d. Wohnungseigentumsgesetz
 Gemersheim, den 2.6. Nov. 2021
 Kreisverwaltung
 Interne Bauverwaltung



ERDGESCHOSS M.1:100

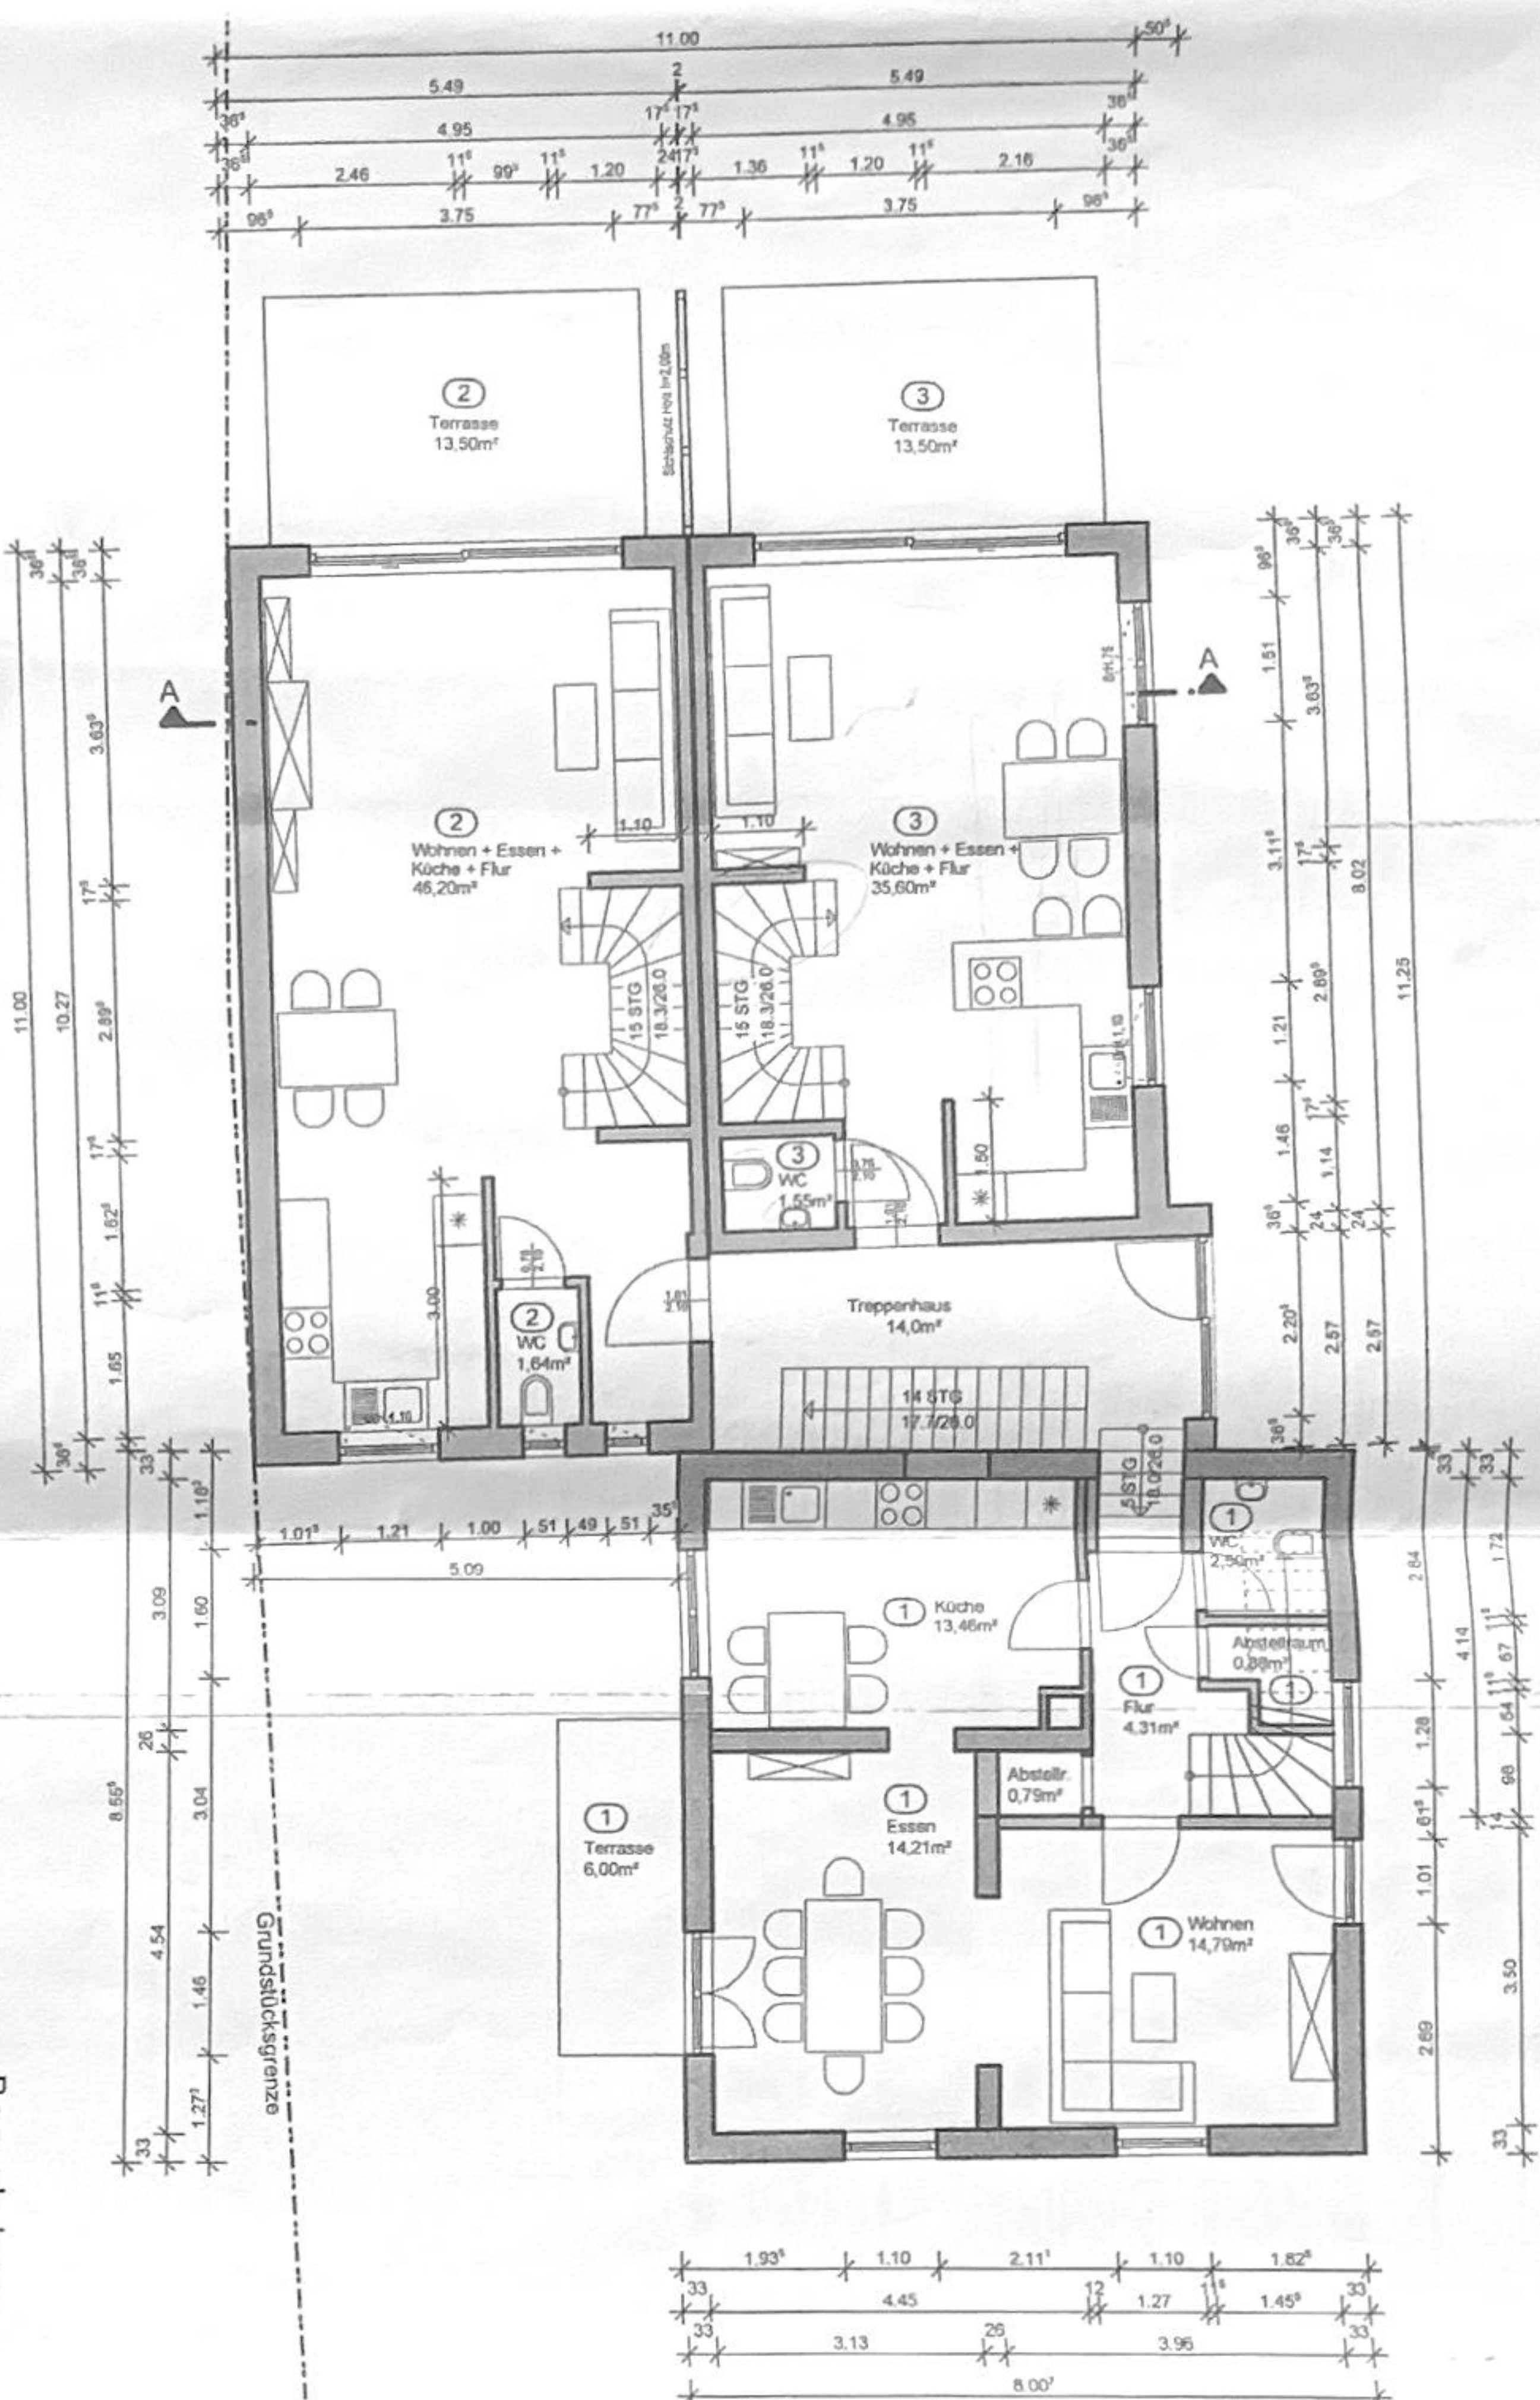

Bauvorhaben :

Umbau und Neubau eines 3-Familienwohnhauses
 Schulstraße 28, 67360 Lingenfeld

Bauherr :

GT Immobilienservice GmbH
 Gemersheimer Straße 150, 67360 Lingenfeld

Planinhalt :

Eingabeplan Grundriss Erdgeschoss

Plan Nr. :

11 Index :

Projektr.:

3518-20

Datum : 09.11.2021

Bearb. : Li

Maßstab : 1:100

Architekt :

Ruthig

RUTHIG Ingenieure
 Ingenieurbüro für Tragwerksplanung

Dipl. Ing. (FH) KP Ruthig
 Von-Denis-Strasse 7
 67346 Speyer
 Tel.: 06232-6790680
 info@ruthig-ingenieure.de

Ausfertigung
Bauherr

Az. 2.1121.12.39.11.13


Bauaufsichtlich geprüft und genehmigt
Germersheim, den 15. Nov. 2021

Kreisverwaltung
Untere Bauaufsichtsbehörde
im Auftrag

[Signature]

Ausfertigungsplan
als Anlage zur Bescheinigung
vom 26. November 2021 § 7 Abs. 4
d. Wohnungseigentumsgesetzes
Germersheim, den 25. Nov. 2021
Kreisverwaltung
Untere Bauaufsichtsbehörde

OBERGESCHOSS M.1:100

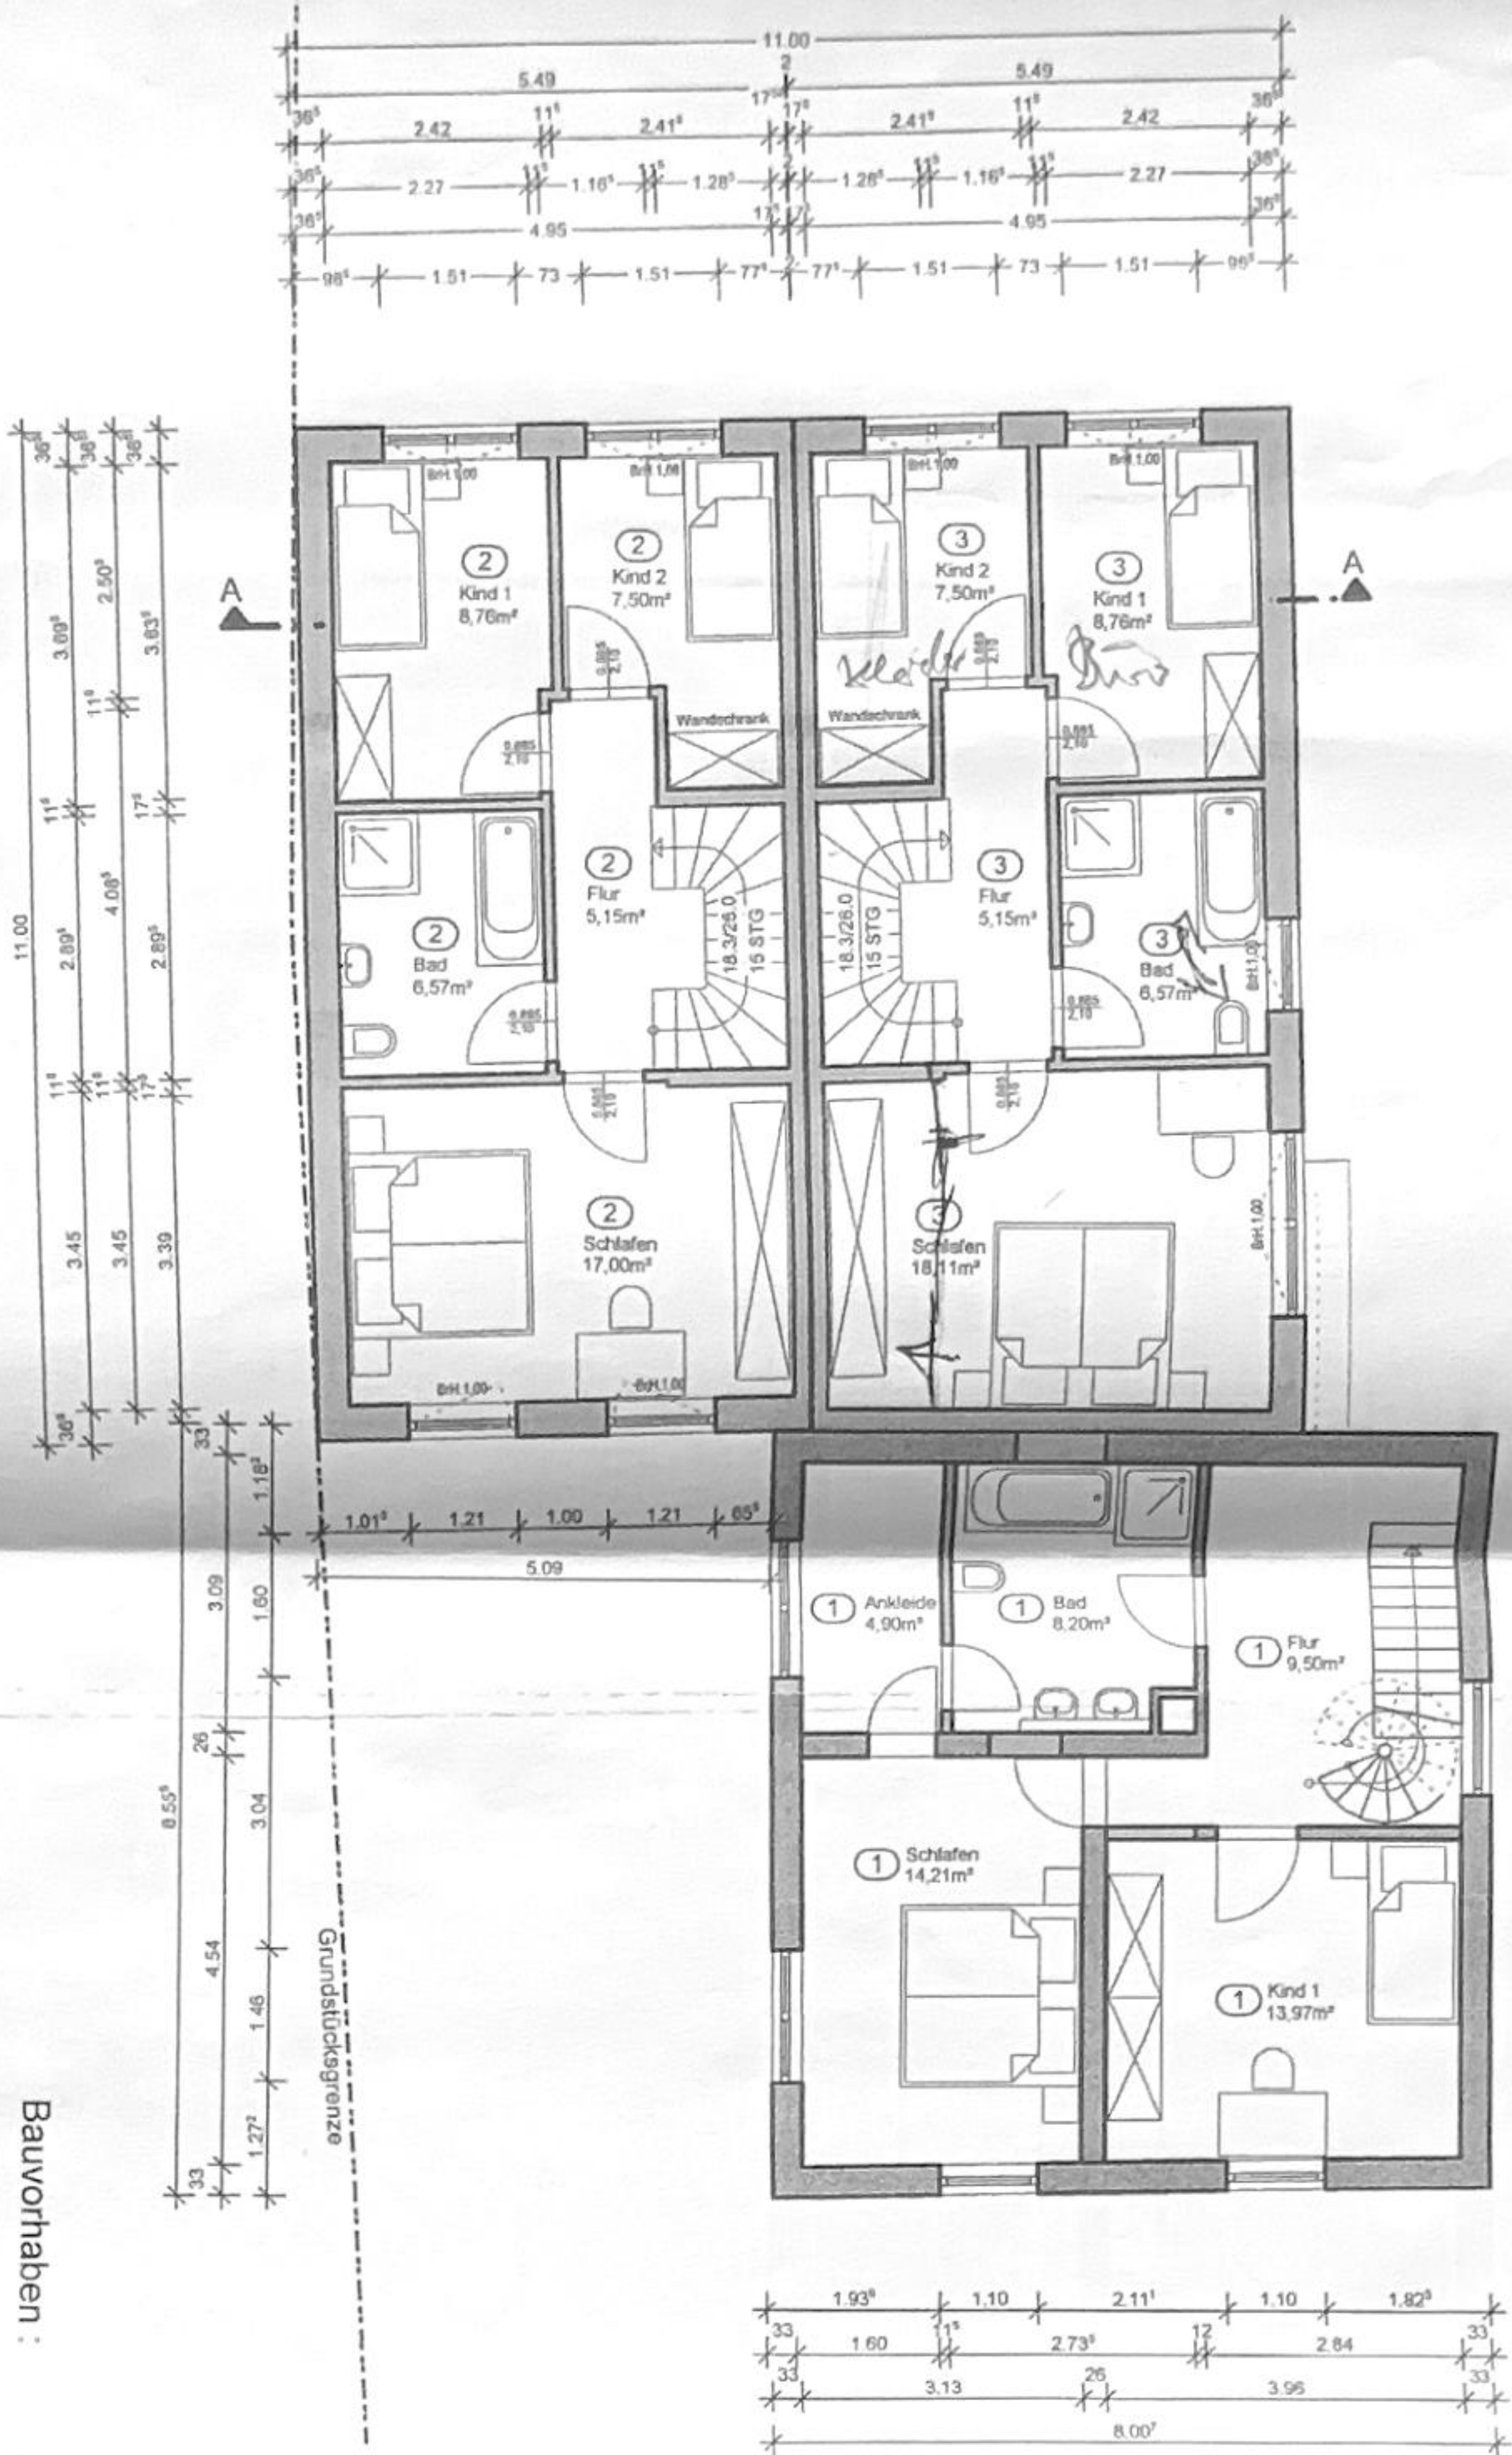

Architekt :

Bauherr :

Bauherr : GT Immobilienservice GmbH
Germersheimer Straße 150, 67360 Lingenfeld


Planinhalt : Eingabeplan Grundriss Obergeschoss

Plan Nr. 12 Index : Datum : 09.11.2021
Bearb. : Li

Projektnr. : 3518-20 Maßstab : 1:100

RUTHIG Ingenieure
Ingenieurbüro für Tragwerksplanung

Dipl.-Ing. (FH) KP. Ruthig
Von-Denis-Strasse 7
67346 Speyer
Tel.: 06232-6790680
info@ruthig-ingenieure.de

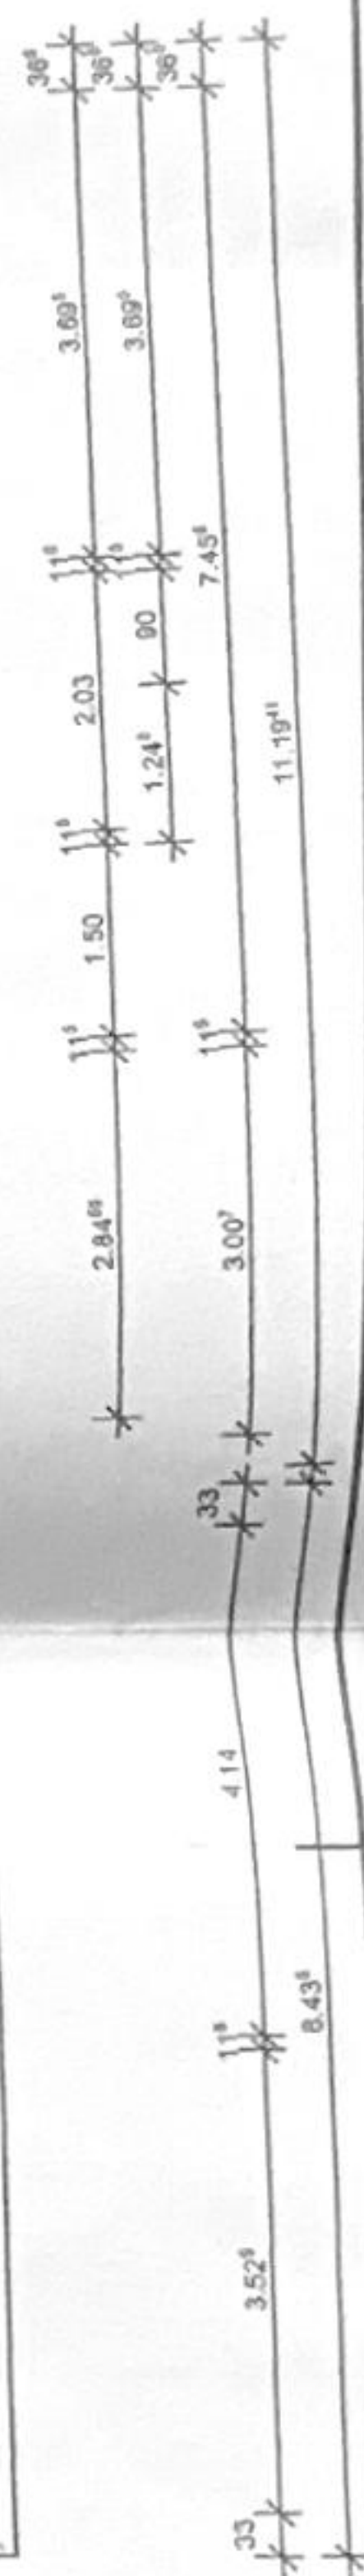


2121 1259/4018

15 Nov 2021

Kreisverwaltung
Unter-B...

Dipl. Ing. (FH) KP. Ruthig
Von-Denis-Strasse 7
67346 Speyer
Tel.: 06232-6790680
info@ruthig-ingenieure.de

SCHNITT A-A

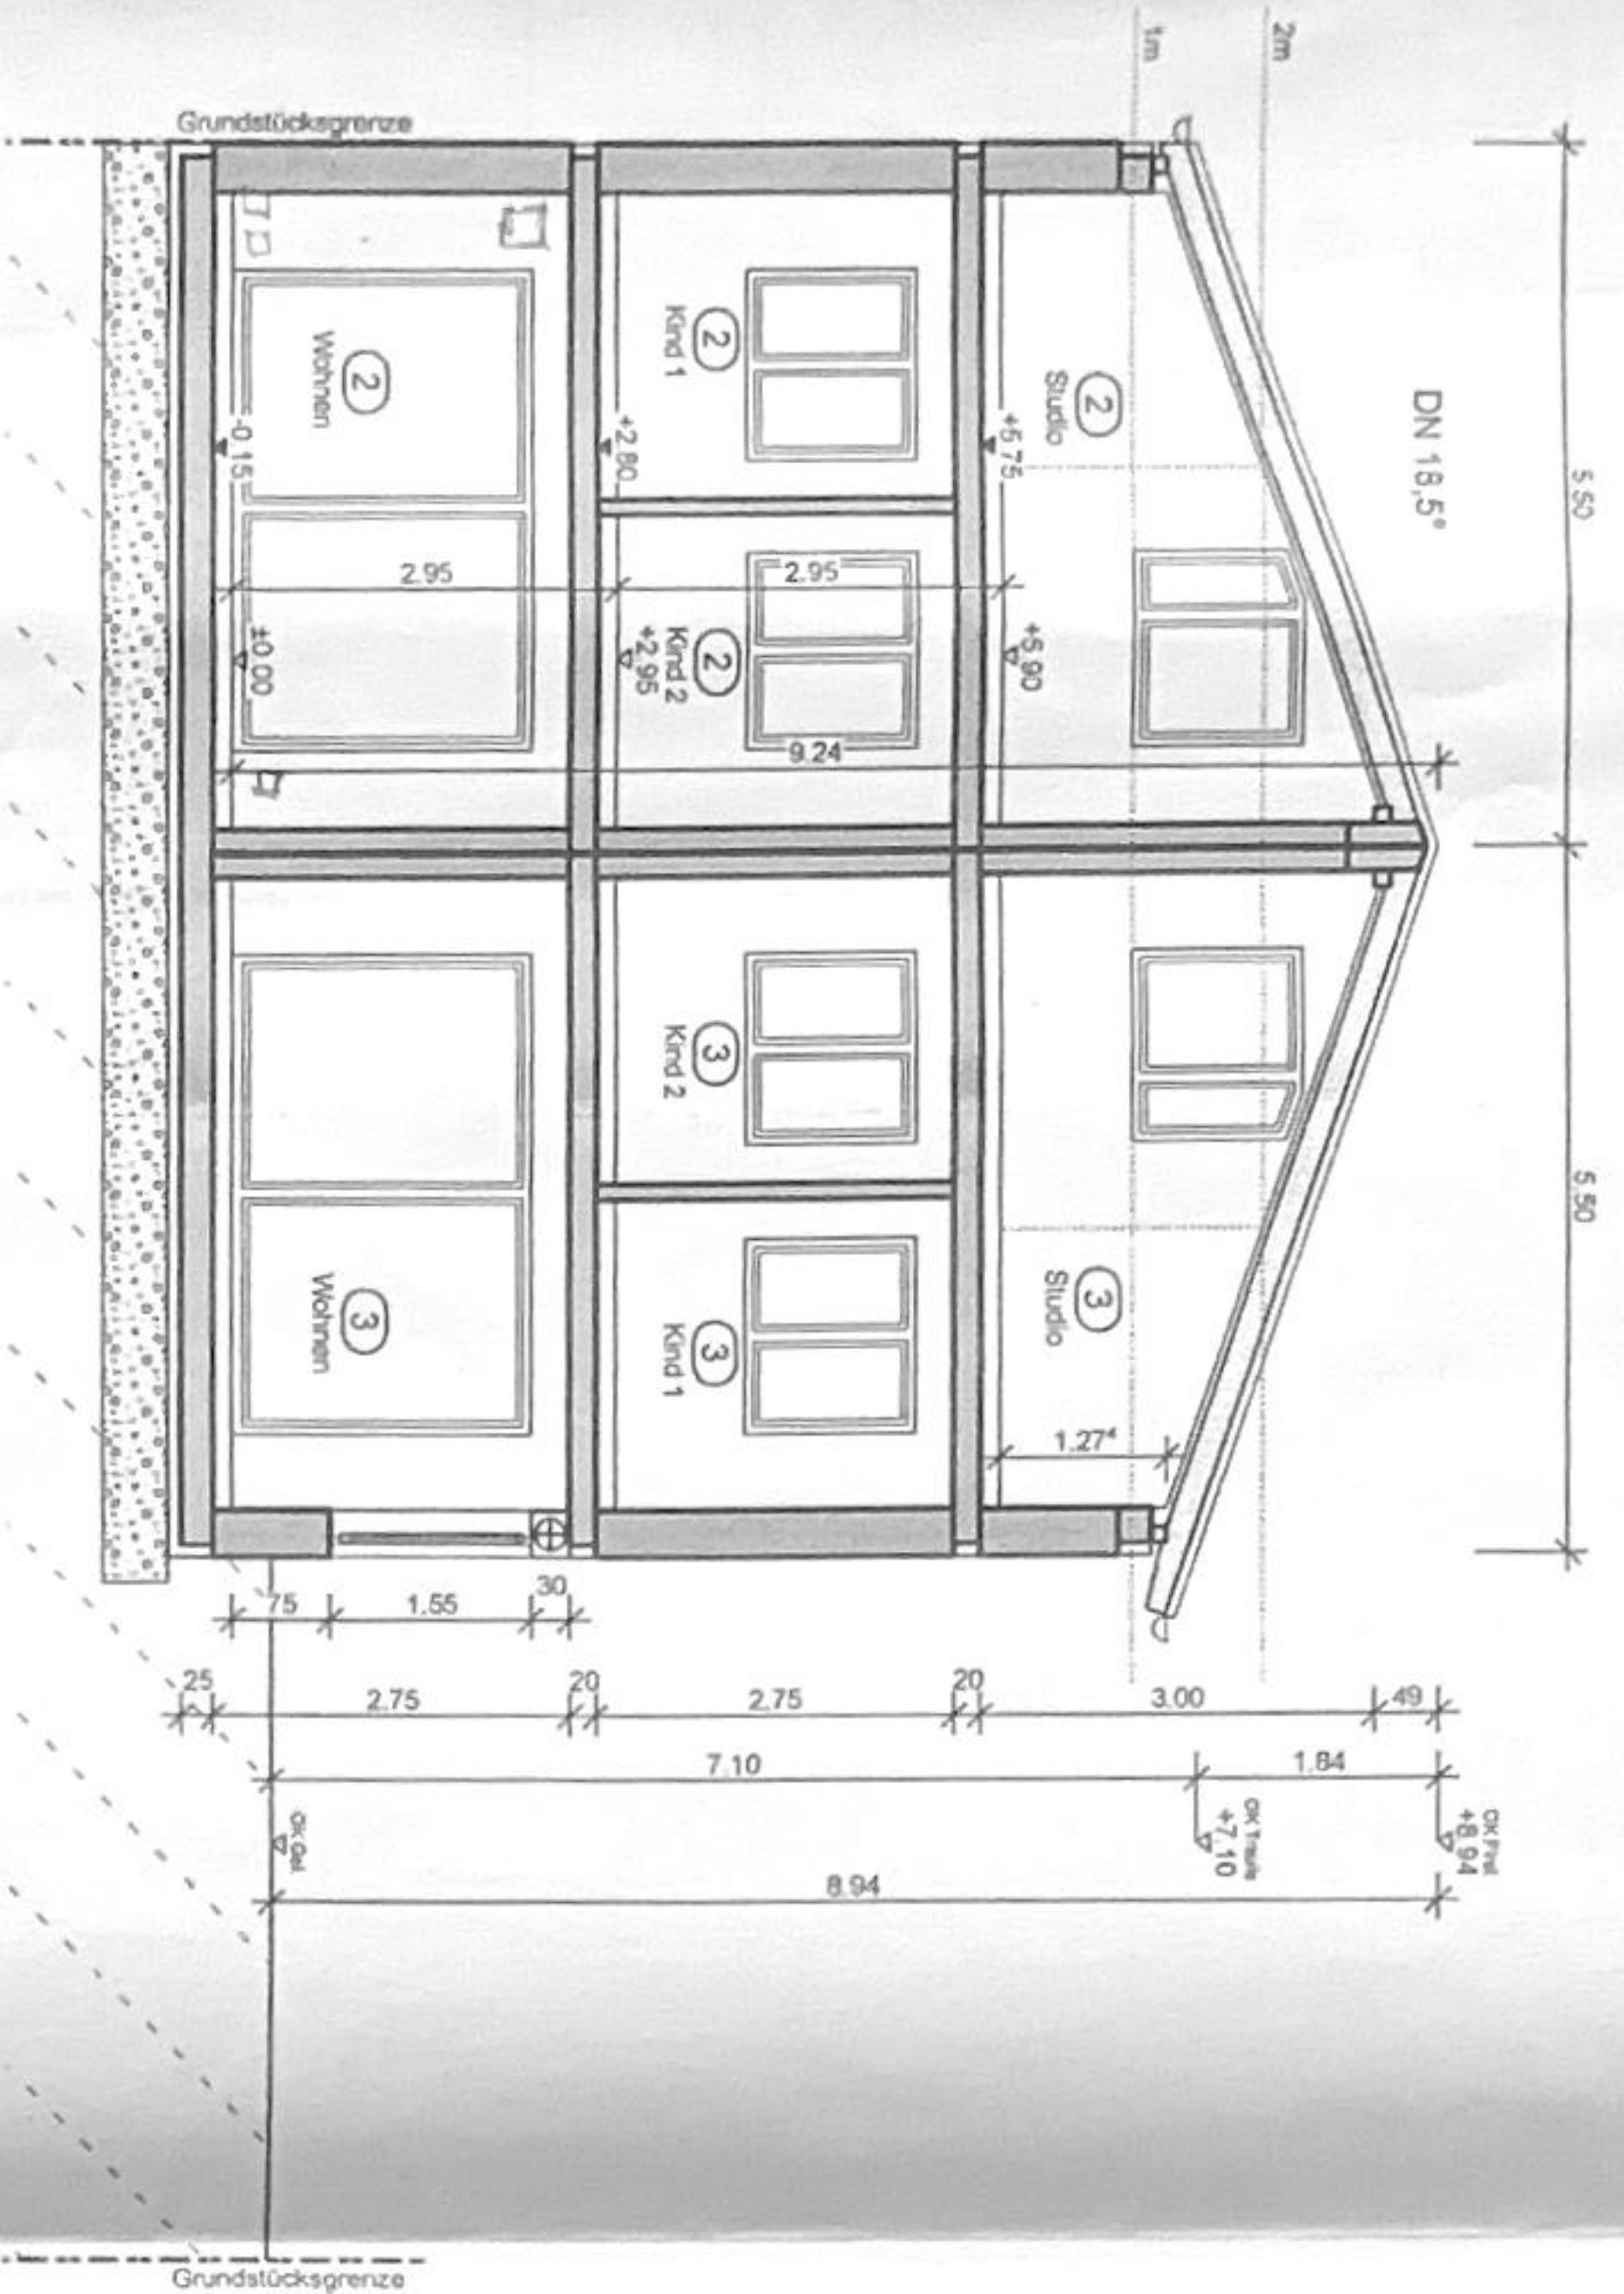

Bauherr:

[Signature]

Architekt:

Ruthig

Bauvorhaben:

Umbau und Neubau eines 3-Familienwohnhauses
Schulstraße 28, 67360 Lingenfeld

Bauherr:

GT Immobilienservice GmbH
Gamersheimer Straße 150, 67360 Lingenfeld

Planinhalt:

Eingabeplan Schnitt

Plan Nr.

30 Index:

Projektnr.:

3518-20

Datum: 09.11.2021

Bearb.: LI

Maßstab: 1:100

Abgefragt für den
Bauherrn

Az.: 21121234/LLP 18
Baufachliche Genehmigung und GEF 2. Handl.
Gamersheim, vom 15. Nov. 2021
Kreisverwaltung
- Untere Bauaufsichtsbehörde -
in Auftrag


als Anlage zur Bescheinigung
vom 26. November 2021 S. 7 Abs. 1
d. Wohnungseigentumsgesetzes
Gemersheim, den 26. Nov. 2021
Kreisverwaltung
Ihre Bauaufsichtsbehörde




RUTHIG Ingenieure
Ingenieurbüro für Tragwerksplanung

Dipl.-Ing. (FH) KP. Ruthig
Von-Denis-Strasse 7
67346 Speyer
Tel.: 06232-6790680
info@ruthig-ingenieure.de

ANSICHT NORD-OST (HOFSEITE)

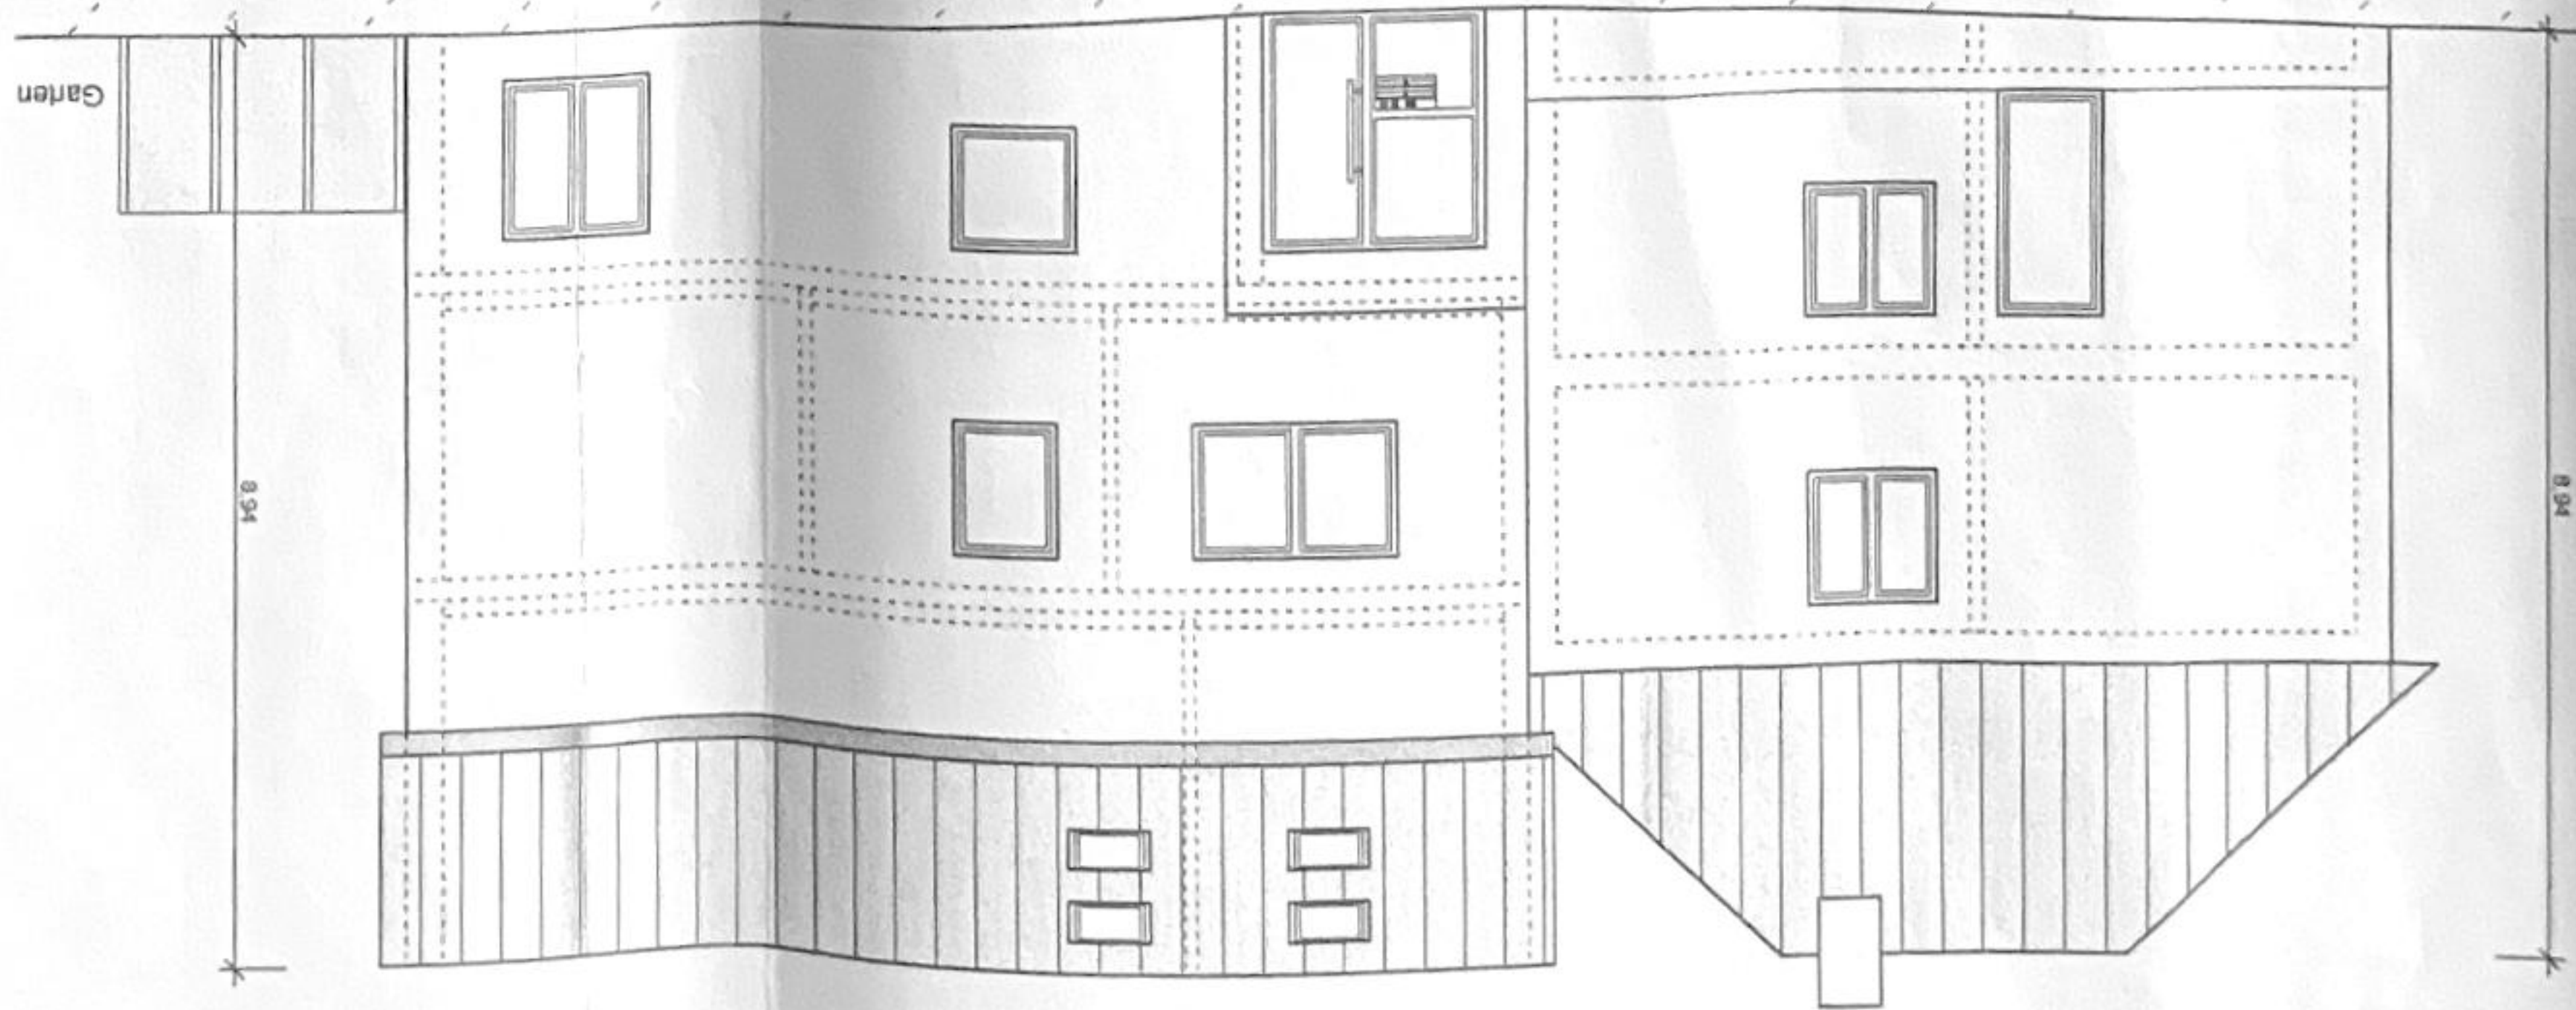

ANSICHT SÜD-OST (STRASSESEITE)

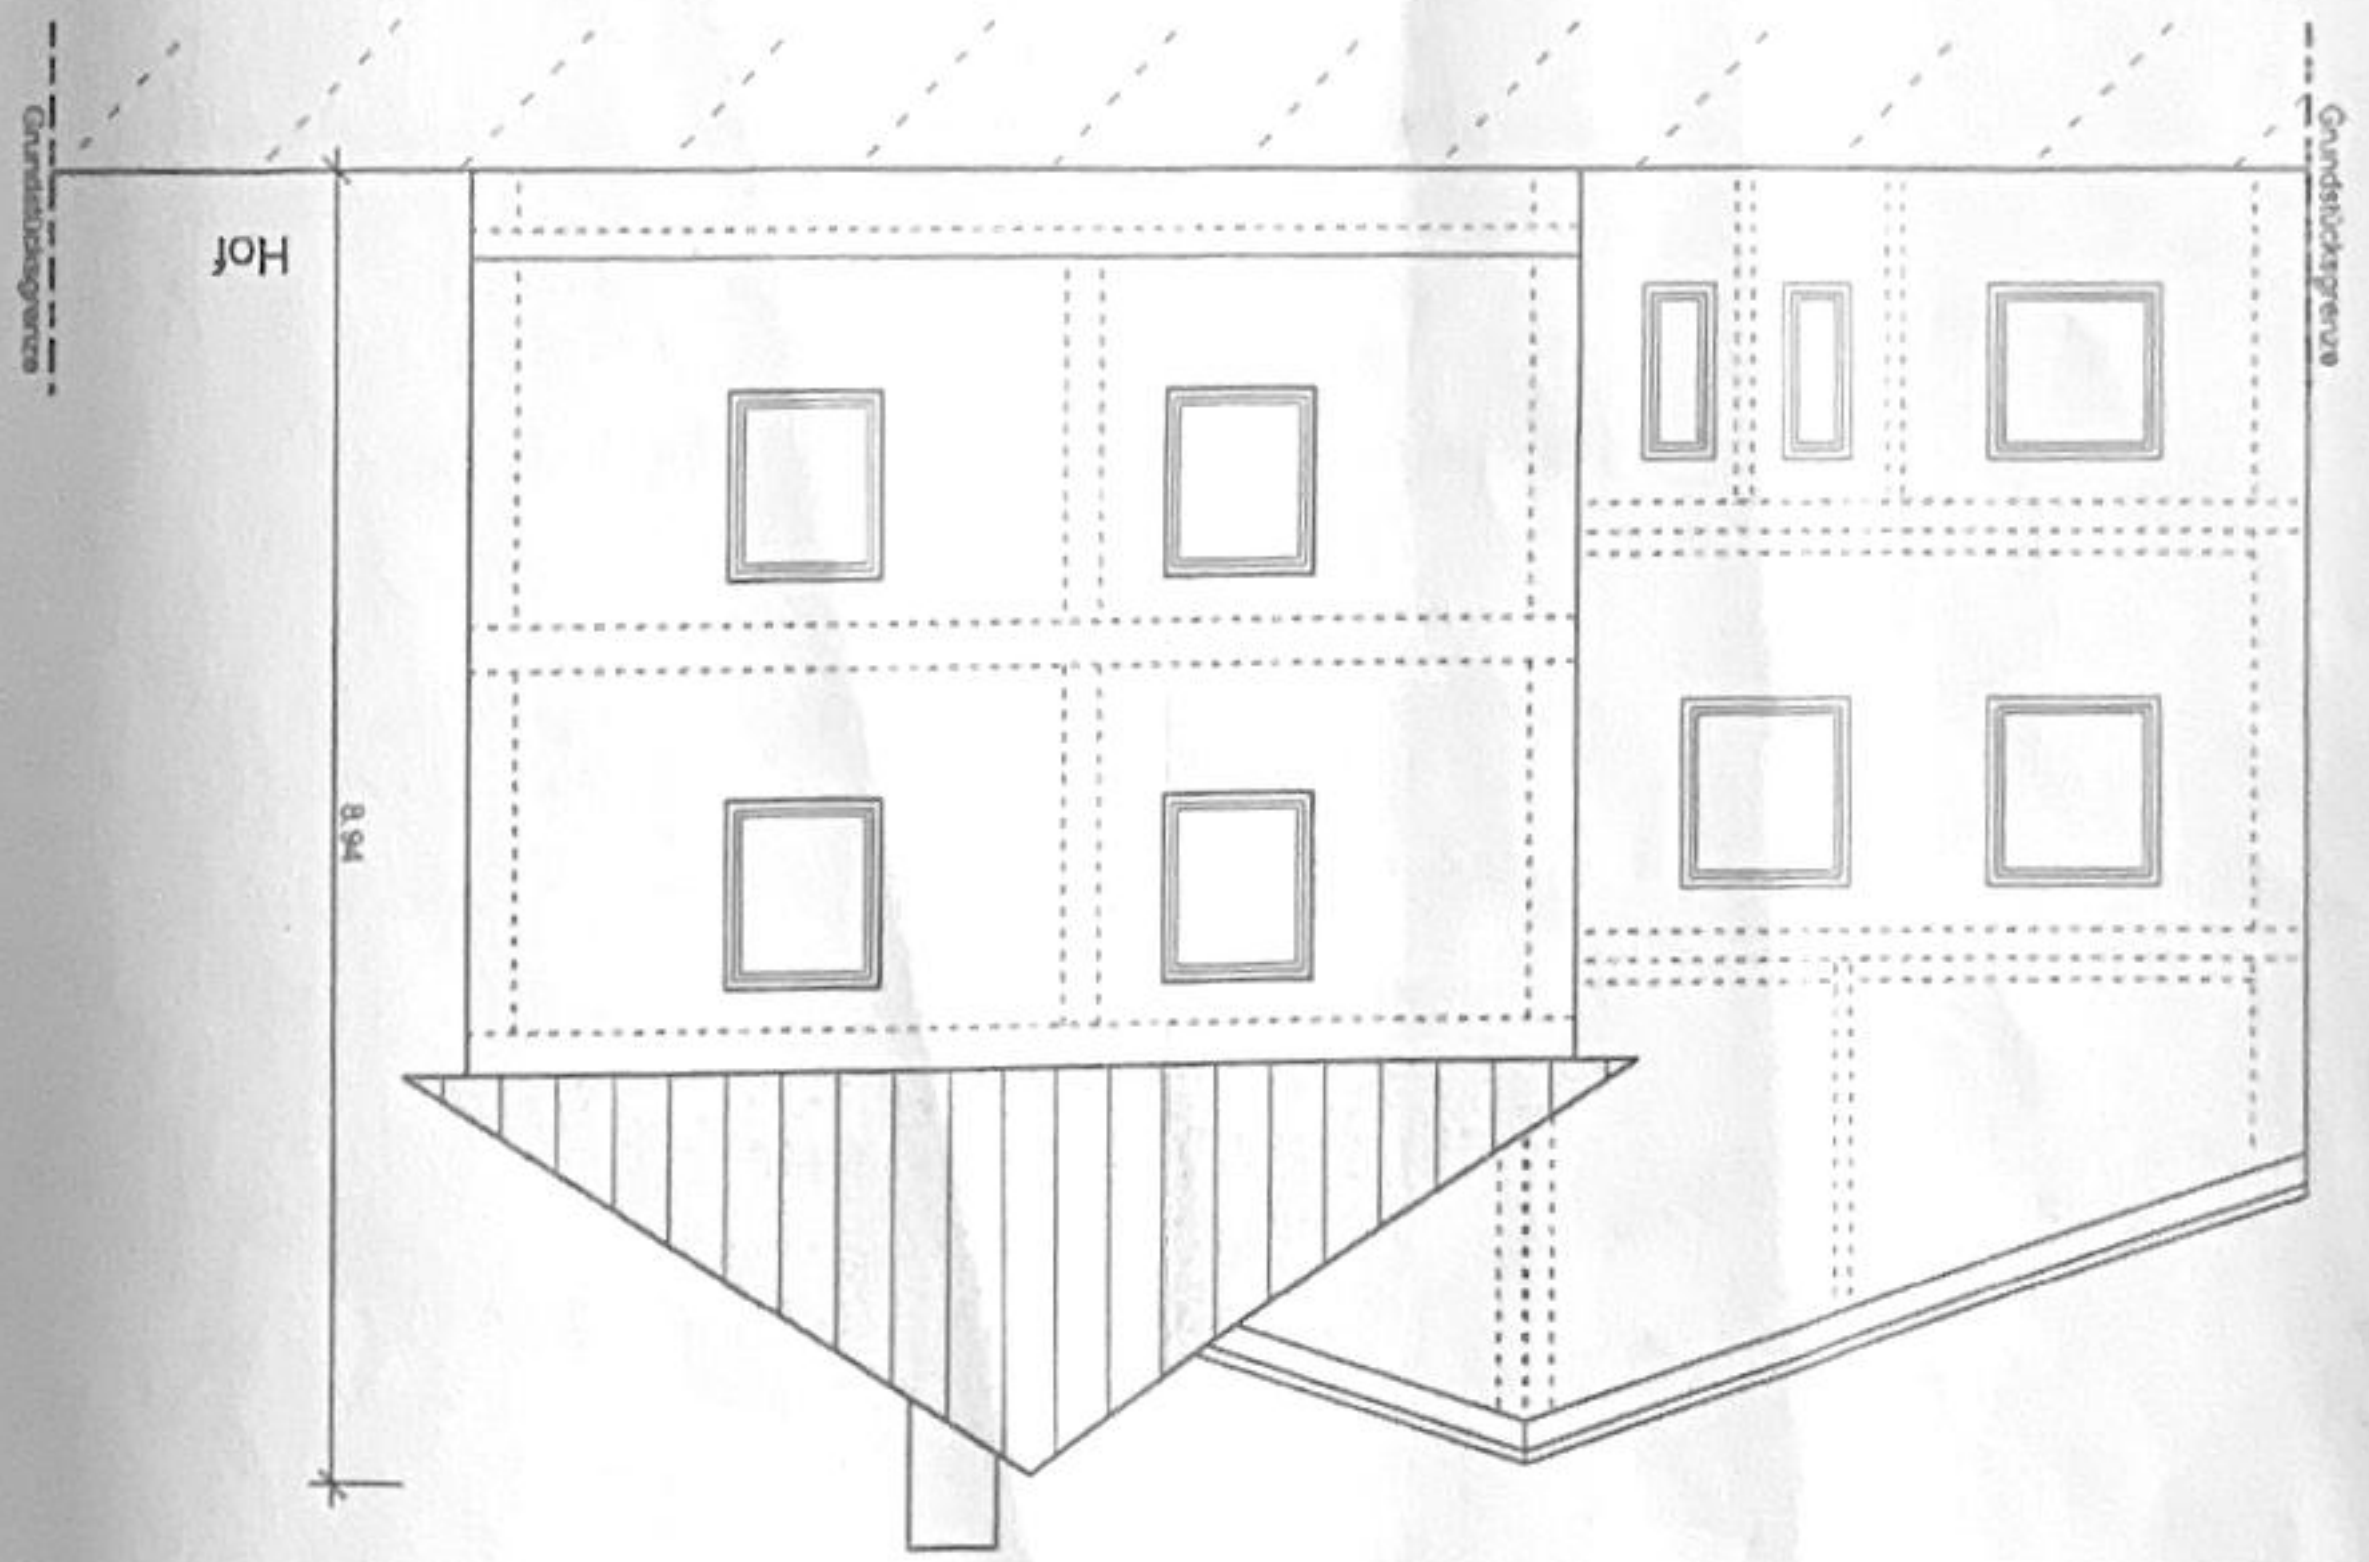

Architekt:

Ruthig

Bauherr:

[Signature]



Ausfertigung:
als Anlage zur Bescheinigung
vom 26. NOV. 2021 § 7 Abs. 1
Wohnungseigentumsgesetz
Garmisch-Partenkirchen, den 26. NOV. 2021
Kreisverwaltung
Untere Bauaufsichtsbehörde

2121 12341413
Gemeinschaftlich Eigentum
Garmisch-Partenkirchen, den 15. NOV. 2021
Kreisverwaltung
Untere Bauaufsichtsbehörde

Ausfertigung für den Bauherrn

Bauvorhaben:

Umbau und Neubau eines 3-Familienwohnhauses
Schulstraße 28, 67360 Lingenfeld

Bauherr:

GT Immobilienservice GmbH
Germersheimer Straße 150, 67360 Lingenfeld

Planinhalt:

Eingabeplan Ansichten NO + SO

Plan Nr.

50

Index:

Datum: 09.11.2021

Bearb.: LI

Maßstab: 1:100


Projektnr.:

3518-20

RUTHIG Ingenieure
Ingenieurbüro für Tragwerksplanung

Dipl.-Ing. (FH) KP. Ruthig
Von-Denis-Strasse 7
67346 Speyer
Tel.: 06232-6790680
info@ruthig-ingenieure.de

ANSICHT SÜD-WEST (GARTENSEITE seitlich)

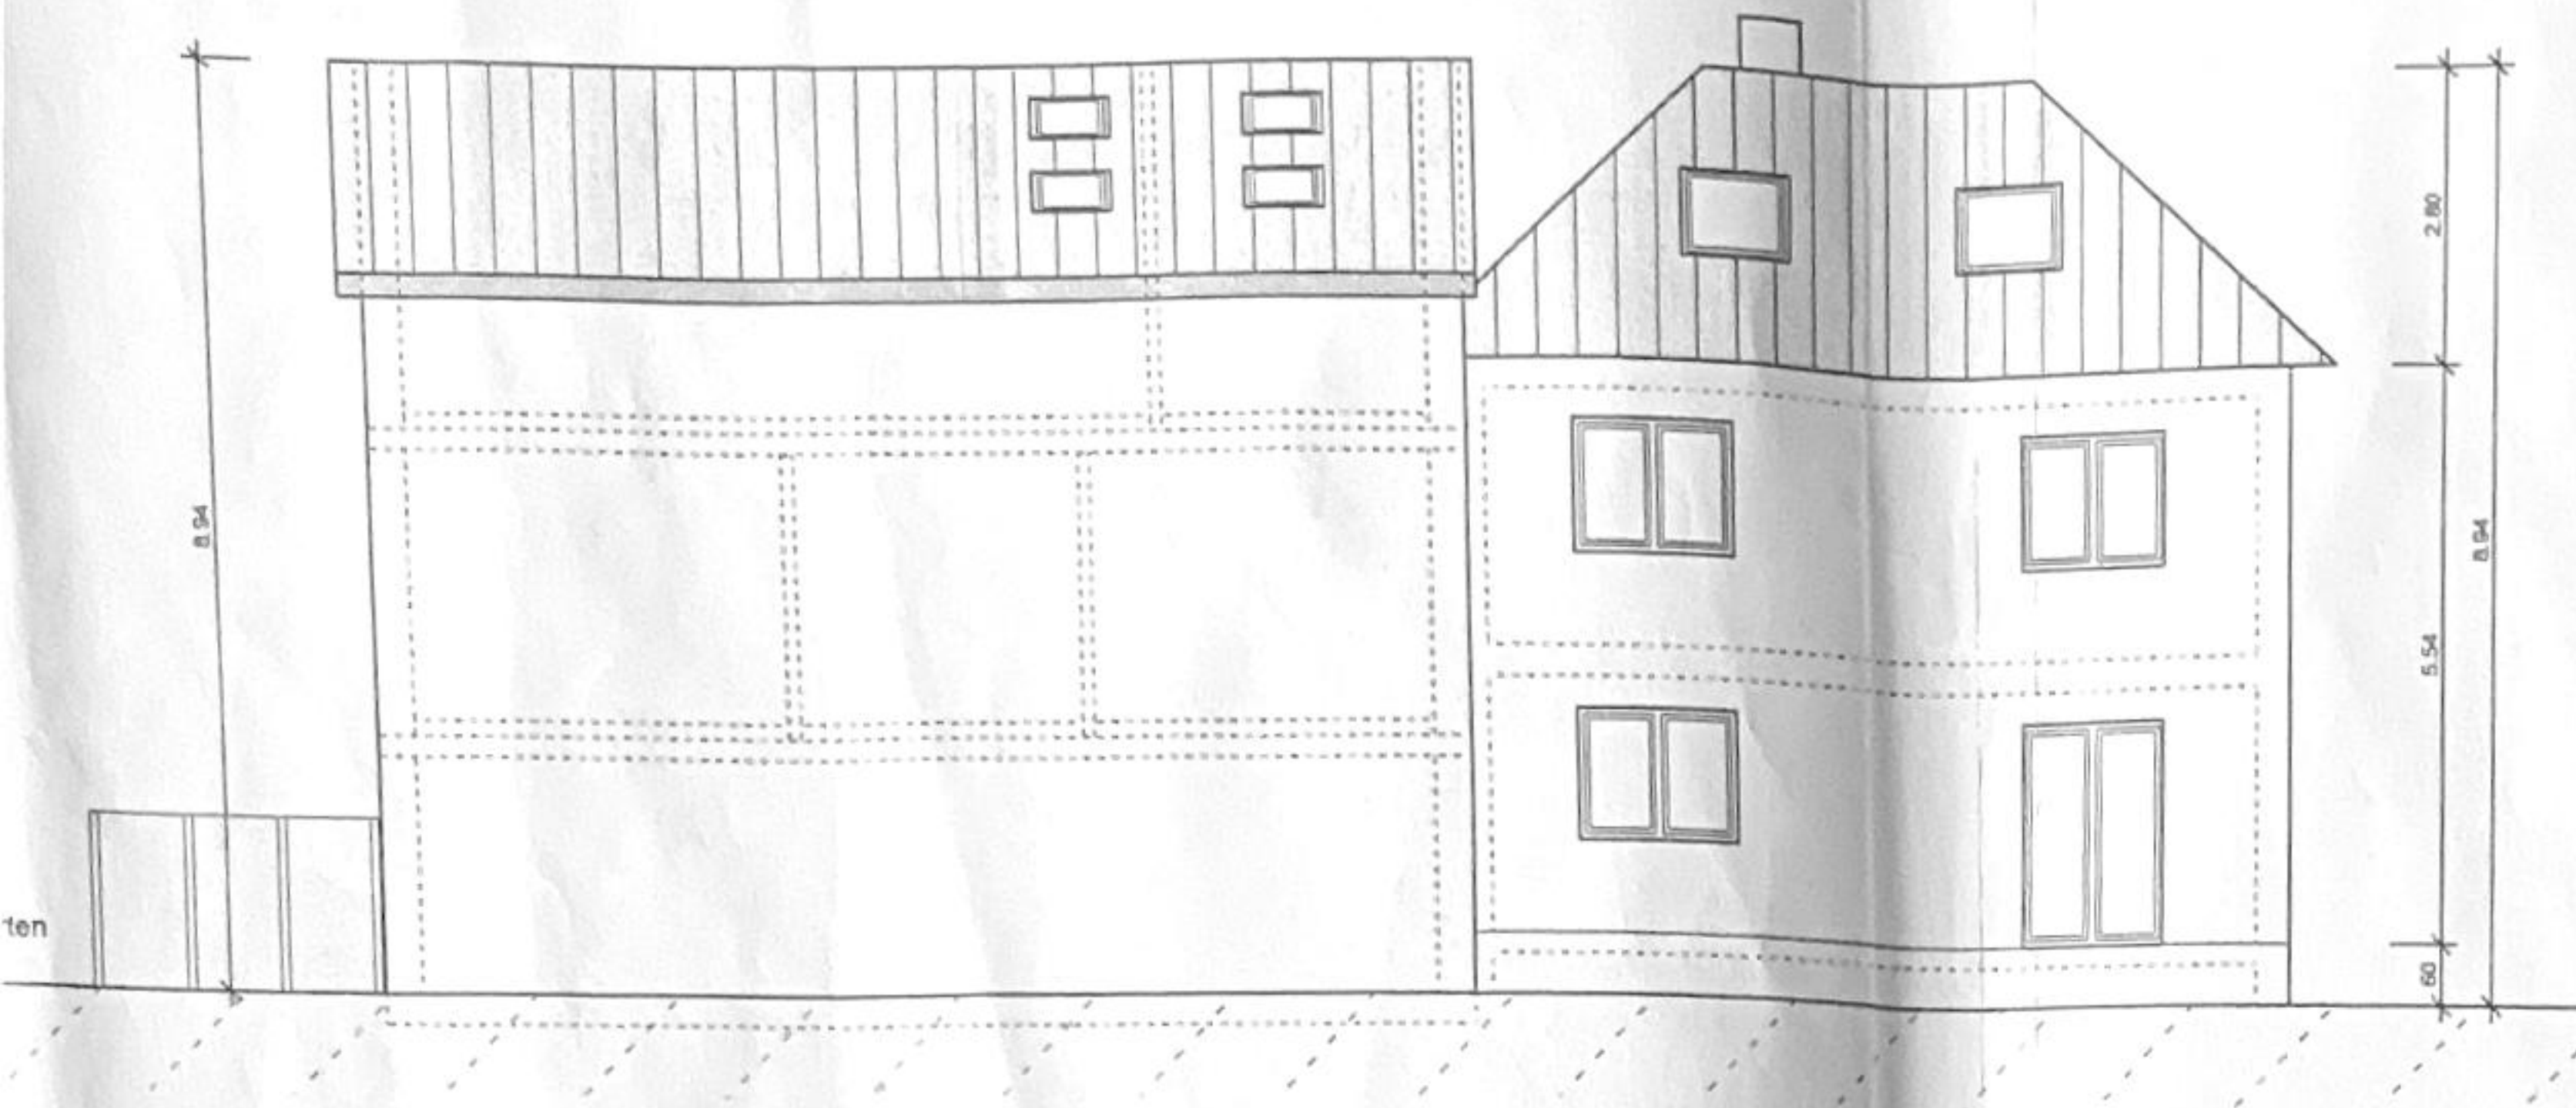

Ausfertigung für den Bauherrn

21/21 1239/41013
Bauaufsichtlich geprüft und genehmigt
Germersheim, den 15. Nov. 2021
Kreisverwaltung
- Untere Bauaufsichtsbehörde -
Im Auftrag

als Anlage zur Bescheinigung
vom 26. Nov. 2021 § 7 Abs. 4
I. Wohnungseigentumsgesetz
Germersheim, den 26. Nov. 2021
Kreisverwaltung
Untere Bauaufsichtsbehörde

Bauherr:

Architekt:

Ruthig

ANSICHT NORD-WEST (GARTENSEITE)



Bauvorhaben: Umbau und Neubau eines 3-Familienwohnhauses
Schulstraße 28, 67360 Lingenfeld

Bauherr: GT Immobilienservice GmbH
Germersheimer Straße 150, 67360 Lingenfeld

Planinhalt: Eingabeplan Ansichten NW + SW

Plan Nr. 51 Index: Datum: 09.11.2021

Projektnr.: 3518-20 Bearb.: Li Maßstab: 1:100

RUTHIG Ingenieure
Ingenieurbüro für Tragwerksplanung

Dipl.-Ing. (FH) KP. Ruthig
Von-Denis-Strasse 7
67346 Speyer

Tel.: 06232-6790680
info@ruthig-ingenieure.de